
PLAN SHEWING PROPERTY
SAID TO BELONG TO

MR. EMMANUEL DASEI DUDARI

ALONG FREDRICK EZENWOSU STREET LOGUDU
KOSOFE LOCAL GOVT AREA
LAGOS STATE
SCALE :- 1:500

10m 5 0 10 20 30m

AREA :- 229.471 SQ MTRS.
ORIGIN :- U. T. M. (ZONE 31)

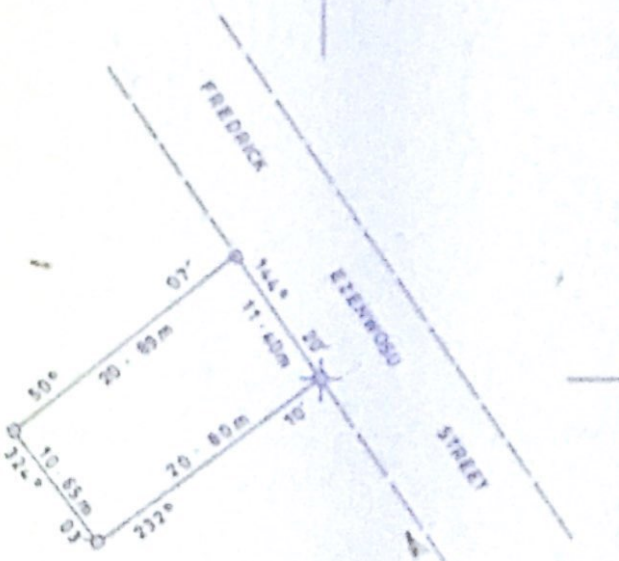

726 363.278 mN


542 718.664 mE

Scanned with CamScanner

PLAN SHEWING PROPERTY
OF
MR. EMMANEL DASEI K. DUDARI
AT OGUDU VILL.
KOSOFE LOCAL GOVT. AREA
LAGOS STATE
SCALE :- 1 : 500

10m 5m 0 10m 20m 30m

AREA :- 823 · 196 SQ. MTS.
ORIGIN :- U.T.M (ZONE 31)

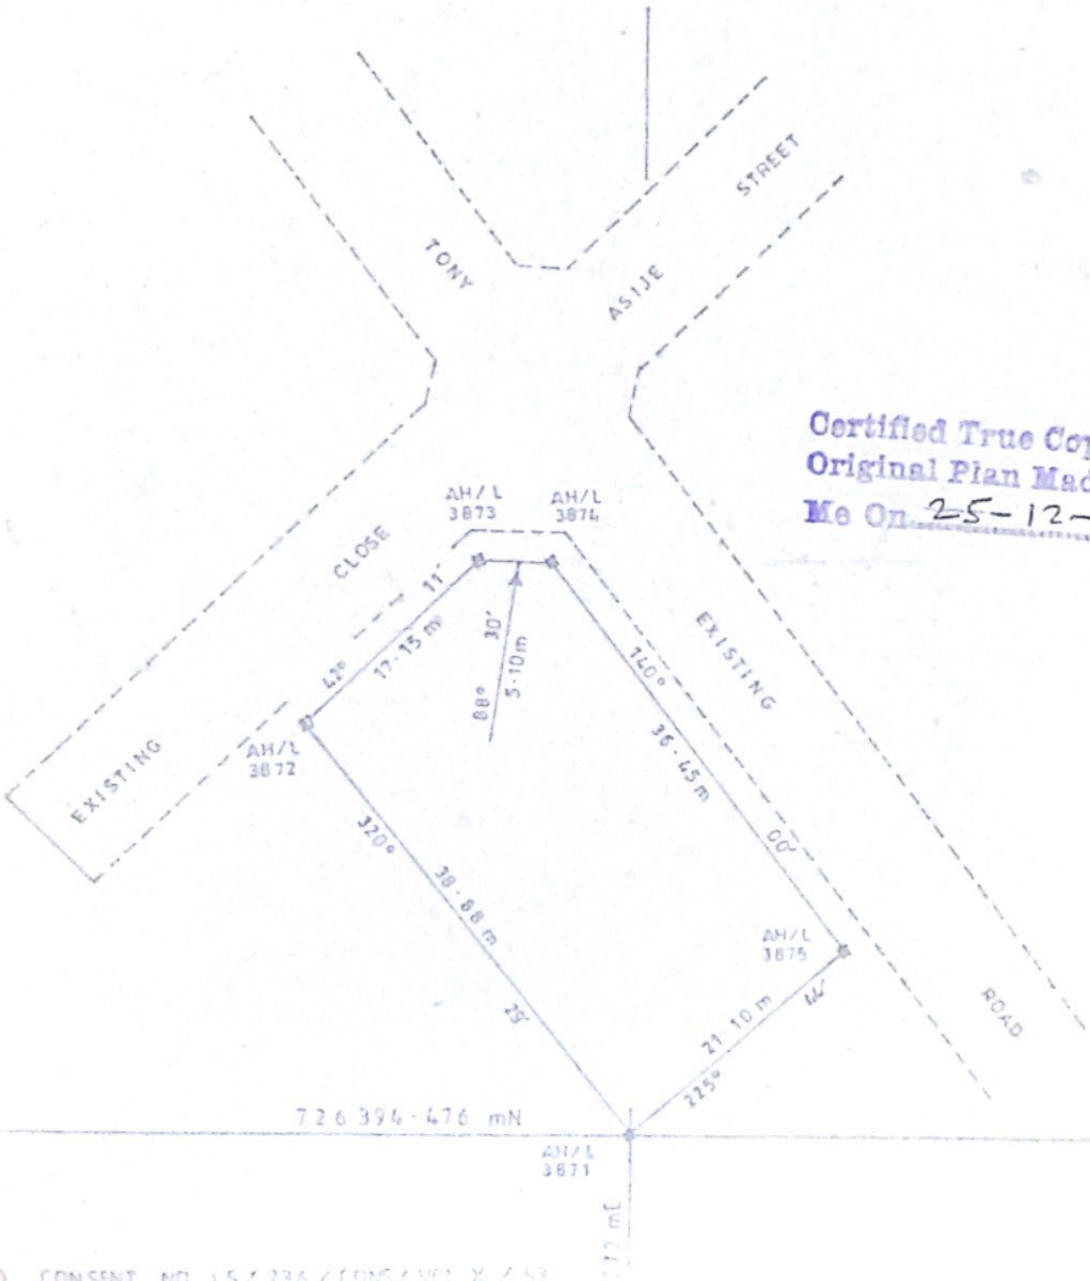

Certified True Copy of
Original Plan Made By
Me On 25-12-2001

APPROVED CONSENT NO. LS/236/CONS/VOL X/52

PLAN NO 100/LS/

Scanned with CamScanner

- PLAN SHEWING PROPERTY -
- SAID TO BELONG TO -

- OSHINGADE OSHINNOWO FAMILY -

- AT EYINRON ODORE IGBONLA VILLAGE EREDO LCDA EPE -
- EPE LOCAL GOVT AREA. -
- LAGOS STATE. -
- SCALE:1:15,000 -

- ORIGIN :- U.T.M.(ZONE 31) -
- AREA:- 849123.081 SQ MTS. (84.912 HECT.) (209.827 ACRES) -

614500.000mE



735397.000mN

ISAAC OLANIYI ADIGUN & ASSOCIATE
OBAFEMI AWOLOWO WAY
BALOGUN B/S. IKEJA LAGOS

CERTIFIED TRUE COPY OF THE
ORIGINAL PLAN MADE BY ME

SURV. ADIGUN I.O M
SURVEYOR
DATE:- 15 - 06 - 202

PLAN NO :- I.O/0495/033G/W/2020/LA



QUEST CONSOLIDATED LTD
Suite 9, Blk B, Second Floor LSPC
Office & Shopping Complex
131, Obafemi Awolowo Way, Alausa
Ikeja, Lagos.
08033788263, 08054473538

Certified True Copy of the Original Plan made by me on 20th July 2023

PLAN NO
ITO/3826/027/2023/LA

20/07/2023.

IGE TAIWO OLUWADAMILARE. Mnis
SURVEYOR

-PLAN SHEWING PROPERTY-

-SAID TO BELONG TO-

MC BUDDY PROPERTIES

-ALONG IGBONLA ROAD, VIA ILARA-

-EPE LOCAL GOVT. AREA-

-LAGOS STATE-

-SCALE: 1:2000-


M20 10 0 40 80 120 160M

-ORIGIN:- U.T.M (ZONE 31)-

-AREA:- 34454.649 SQ.MTS-

-03.445 HECTS & 08.514 ACRES-

PROVISIONAL COPY

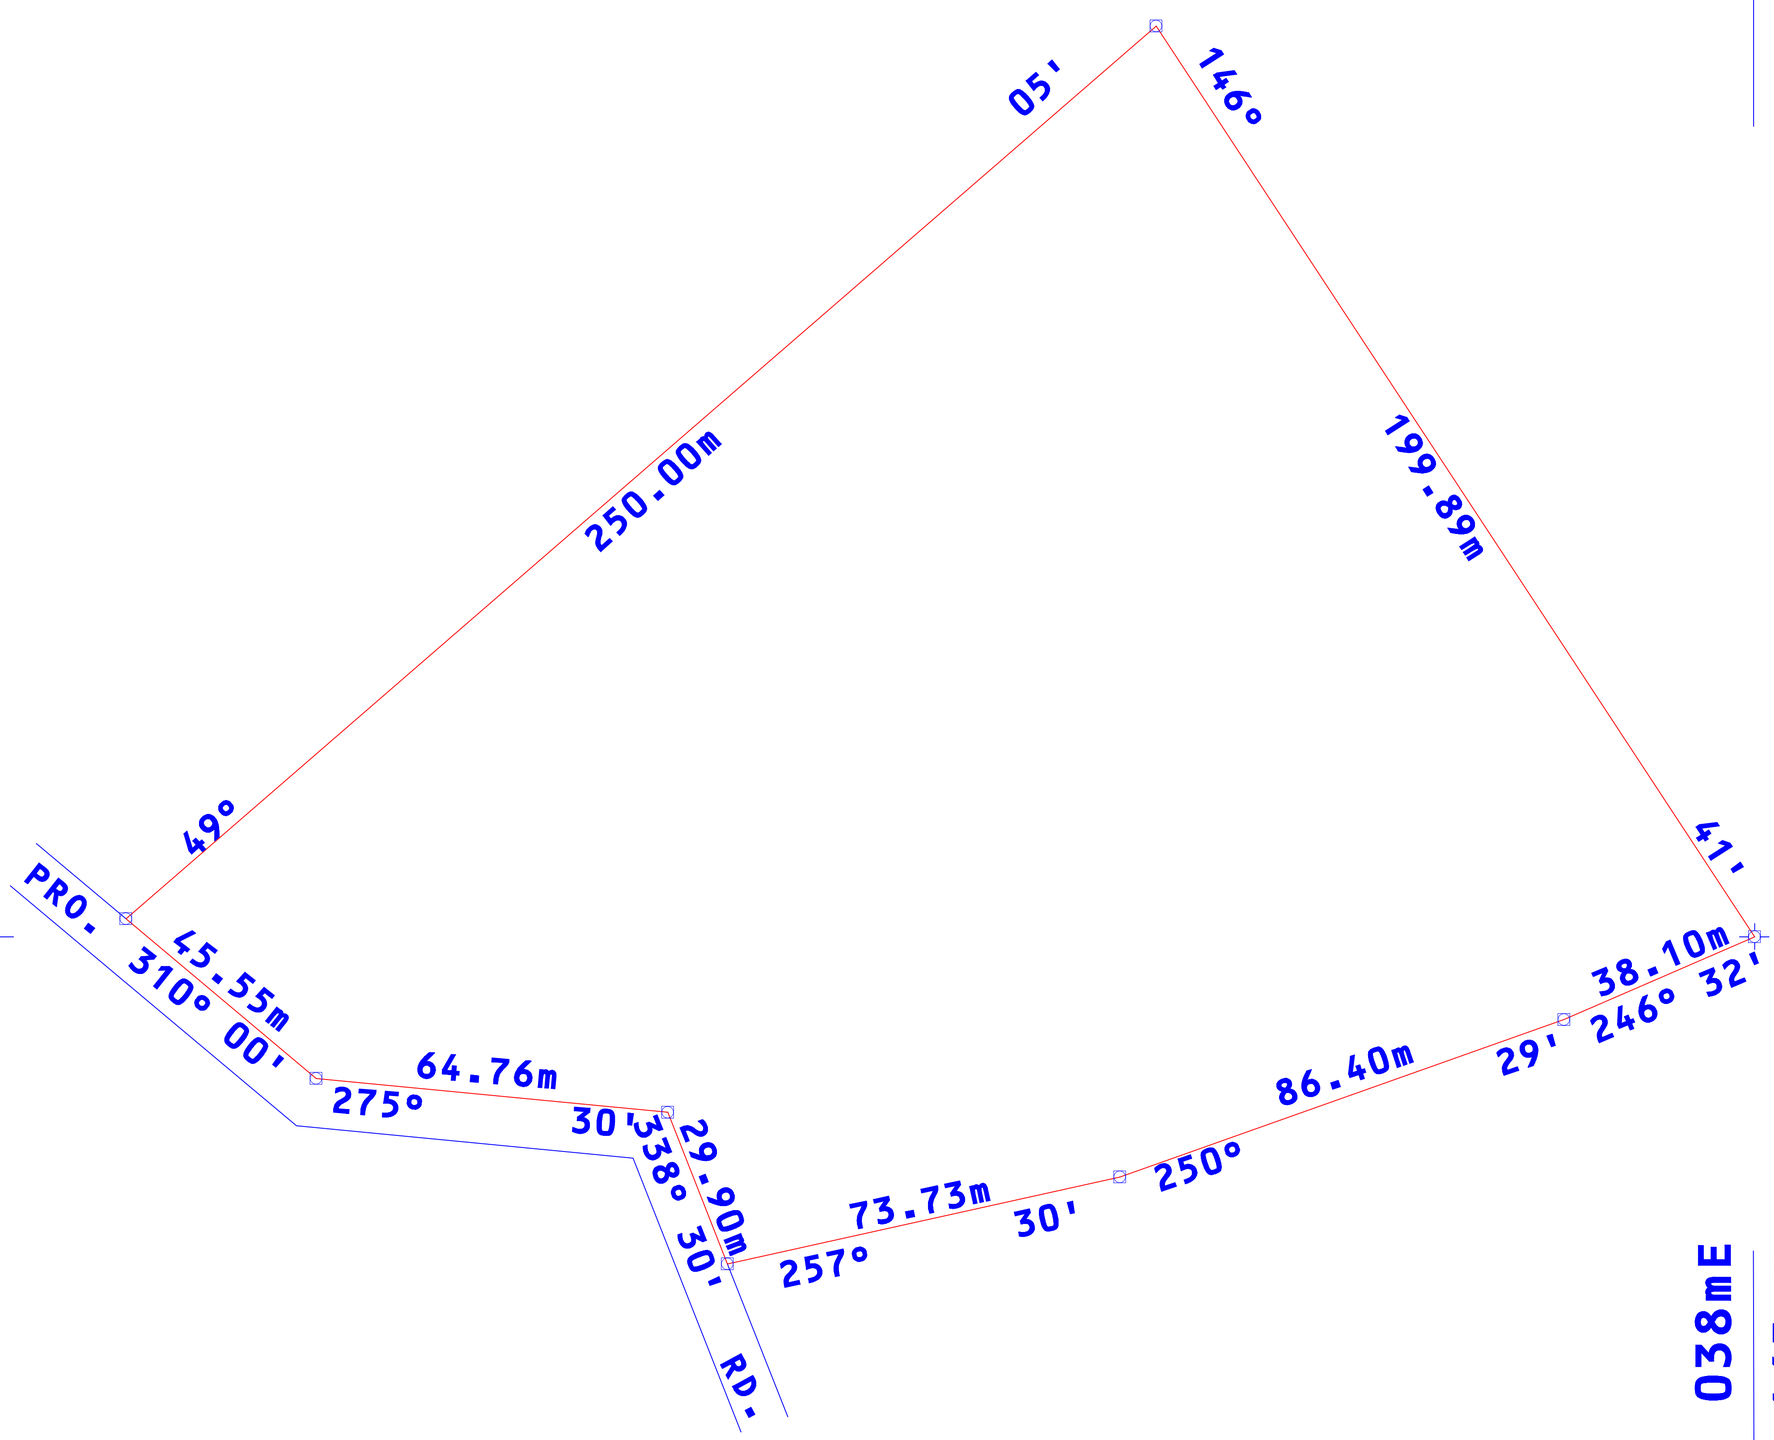

615 027 . 038mE


733 550 . 165mN

U/N

PLAN SHEWING PROPERTY
SAID TO BELONG TO
FIRST ALLY PROPERTIES LIMITED
AT NO. 5, TOLA ADEWUNMI CLOSE, TAAT ESTATE, MARYLAND
IKEJA LOCAL GOVT. AREA
LAGOS STATE

m 0 10 20 40 60 m

SCALE :- 1: 1000
ORIGIN :- U.T.M. (ZONE 31)
AREA :- 2626.683SQ. MTS

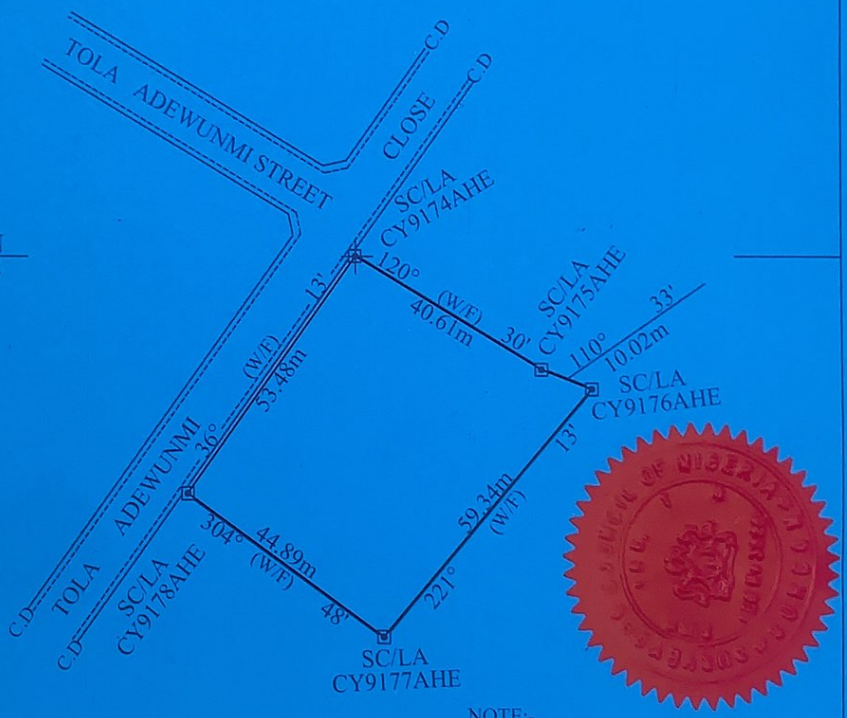

NOTE:-
THIS PLAN SUPERSEDE PLAN NO: ITO/3826/027/2023/LA
MADE BY ME ON 20TH JULY 2023 NOW TITLE CHANGE BY ME


QUEST CONSOLIDATED LTD
Suite 9, Blk B, Second Floor LSPC
Office & Shopping Complex
131, Obafemi Awolowo Way, Alausa
Ikeja, Lagos.
08033788263, 08054473538

Certified True Copy of the Original
Plan made by me on 21st Setember2023


PLAN NO
ITO/3826/038/2023/LA

21/09/2023.

IGE TAIWO OLUWADAMILARE. Mnis
SURVEYOR

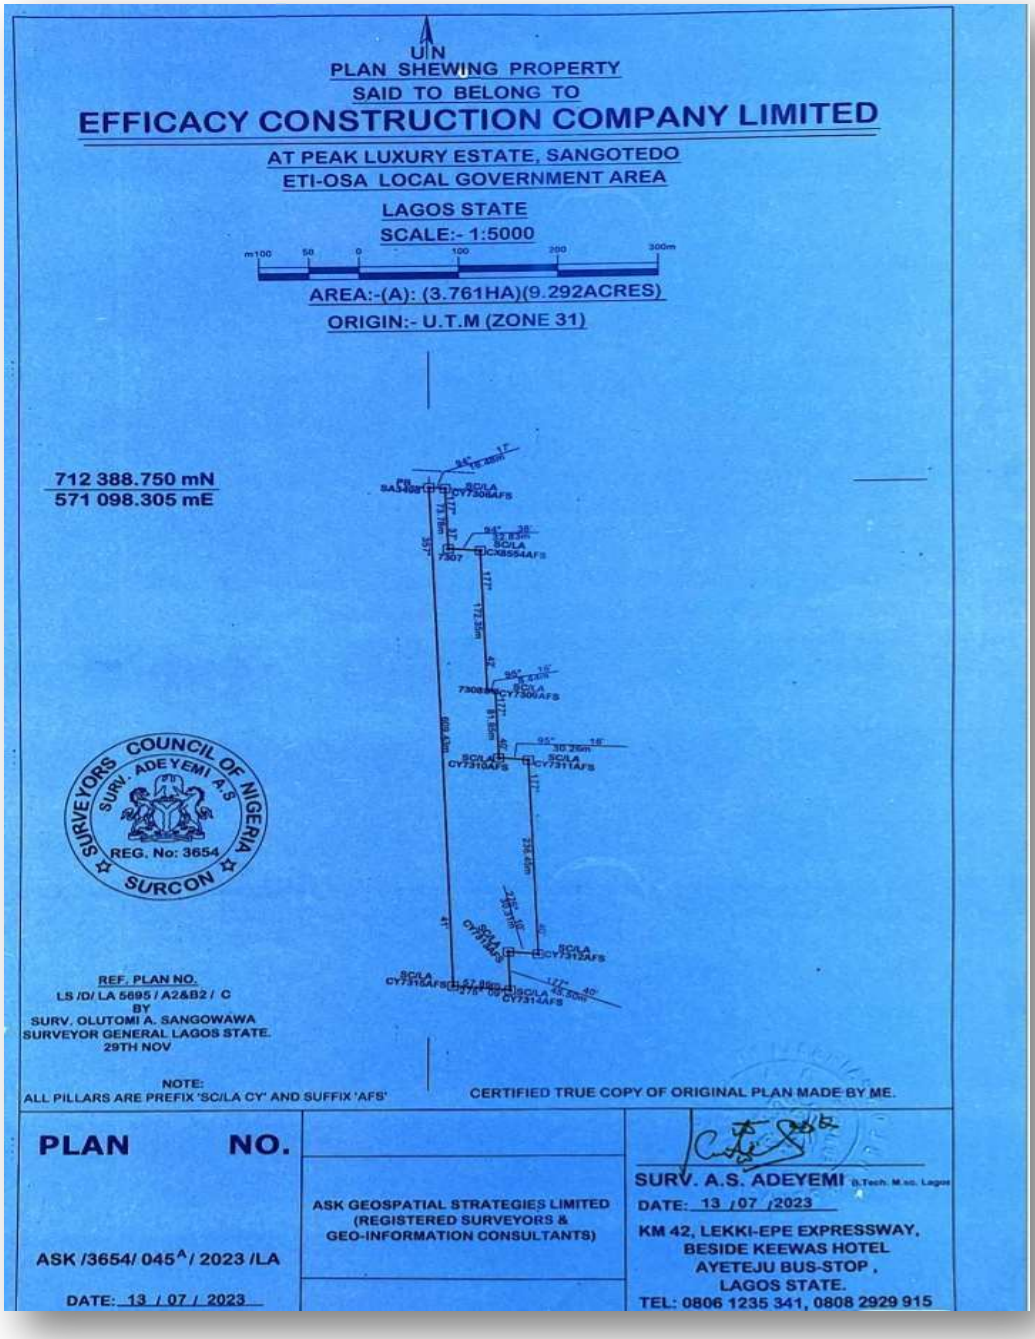

SURVEY PLAN PROVIDED

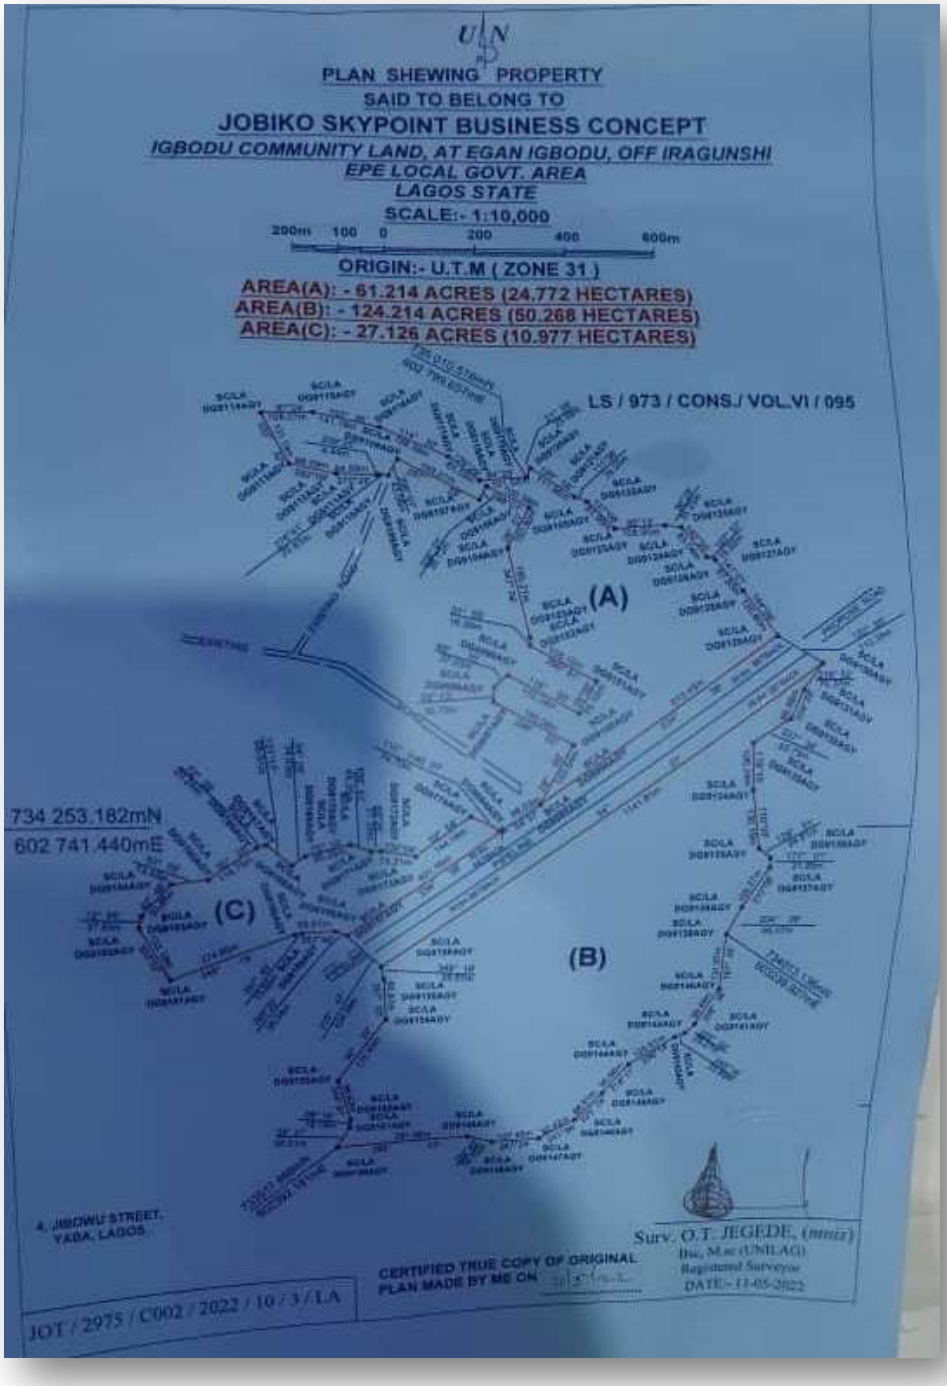

SURVEY PLAN PROVIDED